


“Андижон вилояти Балиқчи туманидаги “Бешкетмон” коллекторини тизимли таъмирлаш ва тиклаш” объекти ишчи лойиҳаси.
Бош режаси.

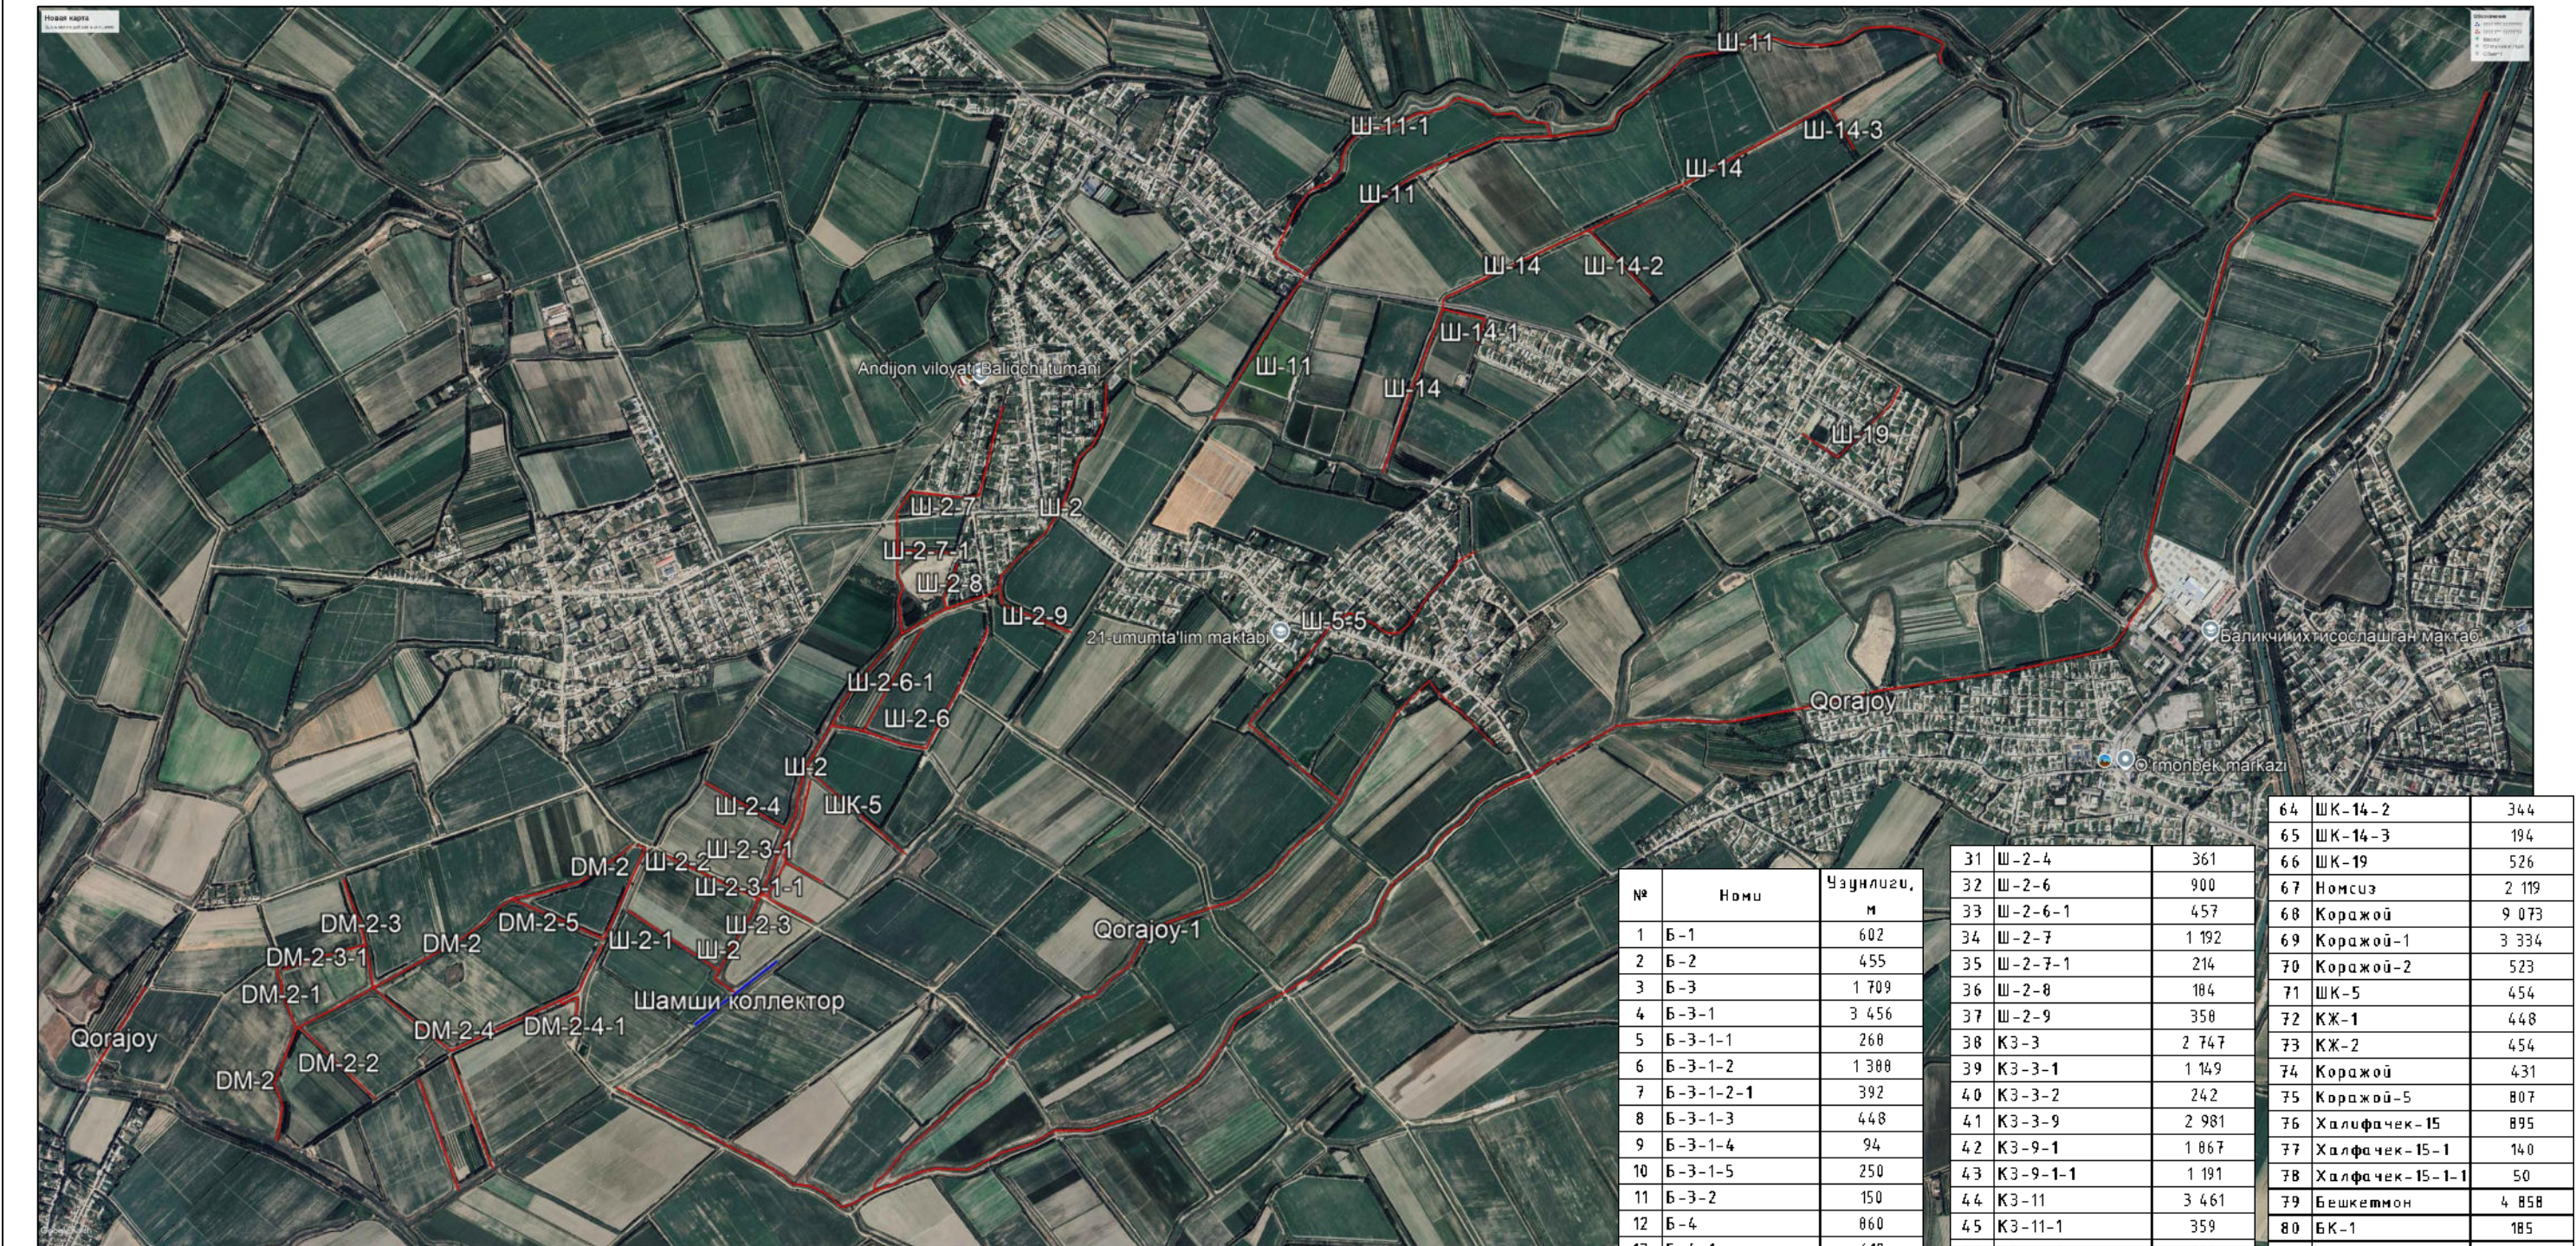

“Андижон вилояти Балиқчи туманидаги “Бешкетмон” коллекторини тизимли таъмирлаш ва тиклаш” объекти ишчи лойиҳаси.						
Изм	Лист	Ф.И.О.	Подпись	Дата	Лист	Листов
ГИП:	Х.Абдухоликов				1	3
Исполнит	У.Йулдошев				000 “INVEST PROYEKT UNIVERSAL”	
Топограф	Ю.Ганиев					

№	Номи	Узунлиги, м
1	Б-1	602
2	Б-2	455
3	Б-3	1 709
4	Б-3-1	3 456
5	Б-3-1-1	268
6	Б-3-1-2	1 388
7	Б-3-1-2-1	392
8	Б-3-1-3	448
9	Б-3-1-4	94
10	Б-3-1-5	250
11	Б-3-2	150
12	Б-4	860
13	Б-4-1	419
14	Б-4-1-1	414
15	Б-5	1 006
16	Б-6	778
17	Б-7	952
18	Б-7-1	177
19	Б-8	550
20	Б-8-1	375
21	Б-9	555
22	Б-9-1	581
23	Б-10	871
24	Б-10-1	570
25	Ш-2	2 961
26	Ш-2-1	419
27	Ш-2-2	394
28	Ш-2-3	224
29	Ш-2-3-1	485
30	Ш-2-3-1-1	159
31	Ш-2-4	361
32	Ш-2-6	900
33	Ш-2-6-1	457
34	Ш-2-7	1 192
35	Ш-2-7-1	214
36	Ш-2-8	184
37	Ш-2-9	358
38	К3-3	2 747
39	К3-3-1	1 149
40	К3-3-2	242
41	К3-3-9	2 981
42	К3-9-1	1 867
43	К3-9-1-1	1 191
44	К3-11	3 461
45	К3-11-1	359
46	К3-11-2	252
47	К3-11-3	227
48	К3-11-3-1	403
49	К3-11-4	280
50	К3-11-5	470
51	К3-14-4	1 842
52	К3-18	2 528
53	К3-18-1	2 165
54	К3-19	2 967
55	К3-19-1	1 301
56	К3-19-1-1	554
57	К3-19-1-2	583
58	К3-19-2	684
59	ШК-5-5	1 524
60	ШК-11	3 547
61	ШК-11-1	1 171
62	ШК-14	2 427
63	ШК-14-1	266
64	ШК-14-2	344
65	ШК-14-3	194
66	ШК-19	526
67	Номсиз	2 119
68	Коражой	9 073
69	Коражой-1	3 334
70	Коражой-2	523
71	ШК-5	454
72	КЖ-1	448
73	КЖ-2	454
74	Коражой	431
75	Коражой-5	807
76	Халифачек-15	895
77	Халифачек-15-1	140
78	Халифачек-15-1-1	50
79	Бешкетмон	4 858
80	БК-1	185
81	БК-2	379
82	БК-4	790
83	БК-5	736
84	БК-6	599
85	БК-7	1 233
86	БК-7-1	740
87	БК-7-2	523
88	БК-8	850
89	БК-9	241
90	ДМ-2	1 946
91	ДМ-2-1	283
92	ДМ-2-2	405
93	ДМ-3-2	437
94	ДМ-3-2-1	331
95	ДМ-3-4	1 119
96	ДМ-3-4-1	223
97	ДМ-2-5	784
Всего		99 270

“Андижон вилояти Балиқчи туманидаги “Бешкетмон” коллекторини тизимли таъмирлаш ва тиклаш” объекти ишчи лойиҳаси.
Бош режаси.




№	Номи	Чуқурлиги, м
1	Б-1	602
2	Б-2	455
3	Б-3	1 709
4	Б-3-1	3 456
5	Б-3-1-1	268
6	Б-3-1-2	1 388
7	Б-3-1-2-1	392
8	Б-3-1-3	448
9	Б-3-1-4	94
10	Б-3-1-5	250
11	Б-3-2	150
12	Б-4	860
13	Б-4-1	419
14	Б-4-1-1	414
15	Б-5	1 006
16	Б-6	778
17	Б-7	952
18	Б-7-1	177
19	Б-8	550
20	Б-8-1	375
21	Б-9	555
22	Б-9-1	581
23	Б-10	871
24	Б-10-1	570
25	Ш-2	2 961
26	Ш-2-1	419
27	Ш-2-2	394
28	Ш-2-3	224
29	Ш-2-3-1	485
30	Ш-2-3-1-1	159

31	Ш-2-4	361
32	Ш-2-6	900
33	Ш-2-6-1	457
34	Ш-2-7	1 192
35	Ш-2-7-1	214
36	Ш-2-8	184
37	Ш-2-9	358
38	КЗ-3	2 747
39	КЗ-3-1	1 149
40	КЗ-3-2	242
41	КЗ-3-9	2 981
42	КЗ-9-1	1 867
43	КЗ-9-1-1	1 191
44	КЗ-11	3 461
45	КЗ-11-1	359
46	КЗ-11-2	252
47	КЗ-11-3	227
48	КЗ-11-3-1	403
49	КЗ-11-4	280
50	КЗ-11-5	470
51	КЗ-14-4	1 842
52	КЗ-18	2 528
53	КЗ-18-1	2 165
54	КЗ-19	2 967
55	КЗ-19-1	1 301
56	КЗ-19-1-1	554
57	КЗ-19-1-2	583
58	КЗ-19-2	684
59	ШК-5-5	1 524
60	ШК-11	3 547
61	ШК-11-1	1 171
62	ШК-14	2 427
63	ШК-14-1	266

64	ШК-14-2	344
65	ШК-14-3	194
66	ШК-19	526
67	Номсуз	2 119
68	Коражой	9 073
69	Коражой-1	3 334
70	Коражой-2	523
71	ШК-5	454
72	КЖ-1	448
73	КЖ-2	454
74	Коражой	431
75	Коражой-5	807
76	Халифачек-15	895
77	Халифачек-15-1	140
78	Халифачек-15-1-1	50
79	Бешкетмон	4 858
80	БК-1	185
81	БК-2	379
82	БК-4	790
83	БК-5	736
84	БК-6	599
85	БК-7	1 233
86	БК-7-1	740
87	БК-7-2	523
88	БК-8	850
89	БК-9	241
90	ДМ-2	1 946
91	ДМ-2-1	283
92	ДМ-2-2	405
93	ДМ-3-2	437
94	ДМ-3-2-1	331
95	ДМ-3-4	1 119
96	ДМ-3-4-1	223
97	ДМ-2-5	784
Всего		99 270

					“Андижон вилояти Балиқчи туманидаги “Бешкетмон” коллекторини тизимли таъмирлаш ва тиклаш” объекти ишчи лойиҳаси.			
Изм	Лист	Ф.И.О.	Подпись	Дата	ГЕН ПЛАН	Лист	Листов	Масштаб
ГИП:		Х.Абдухоликов				2	3	
Исполнит		У.Йулдошев						
Топограф		Ю.Ганиев						
					000 “INVEST PROYEKT UNIVERSAL”			

“Андижон вилояти Балиқчи туманидаги “Бешкетмон” коллекторини тизимли таъмирлаш ва тиклаш” объекти ишчи лойиҳаси.
Бош режаси.

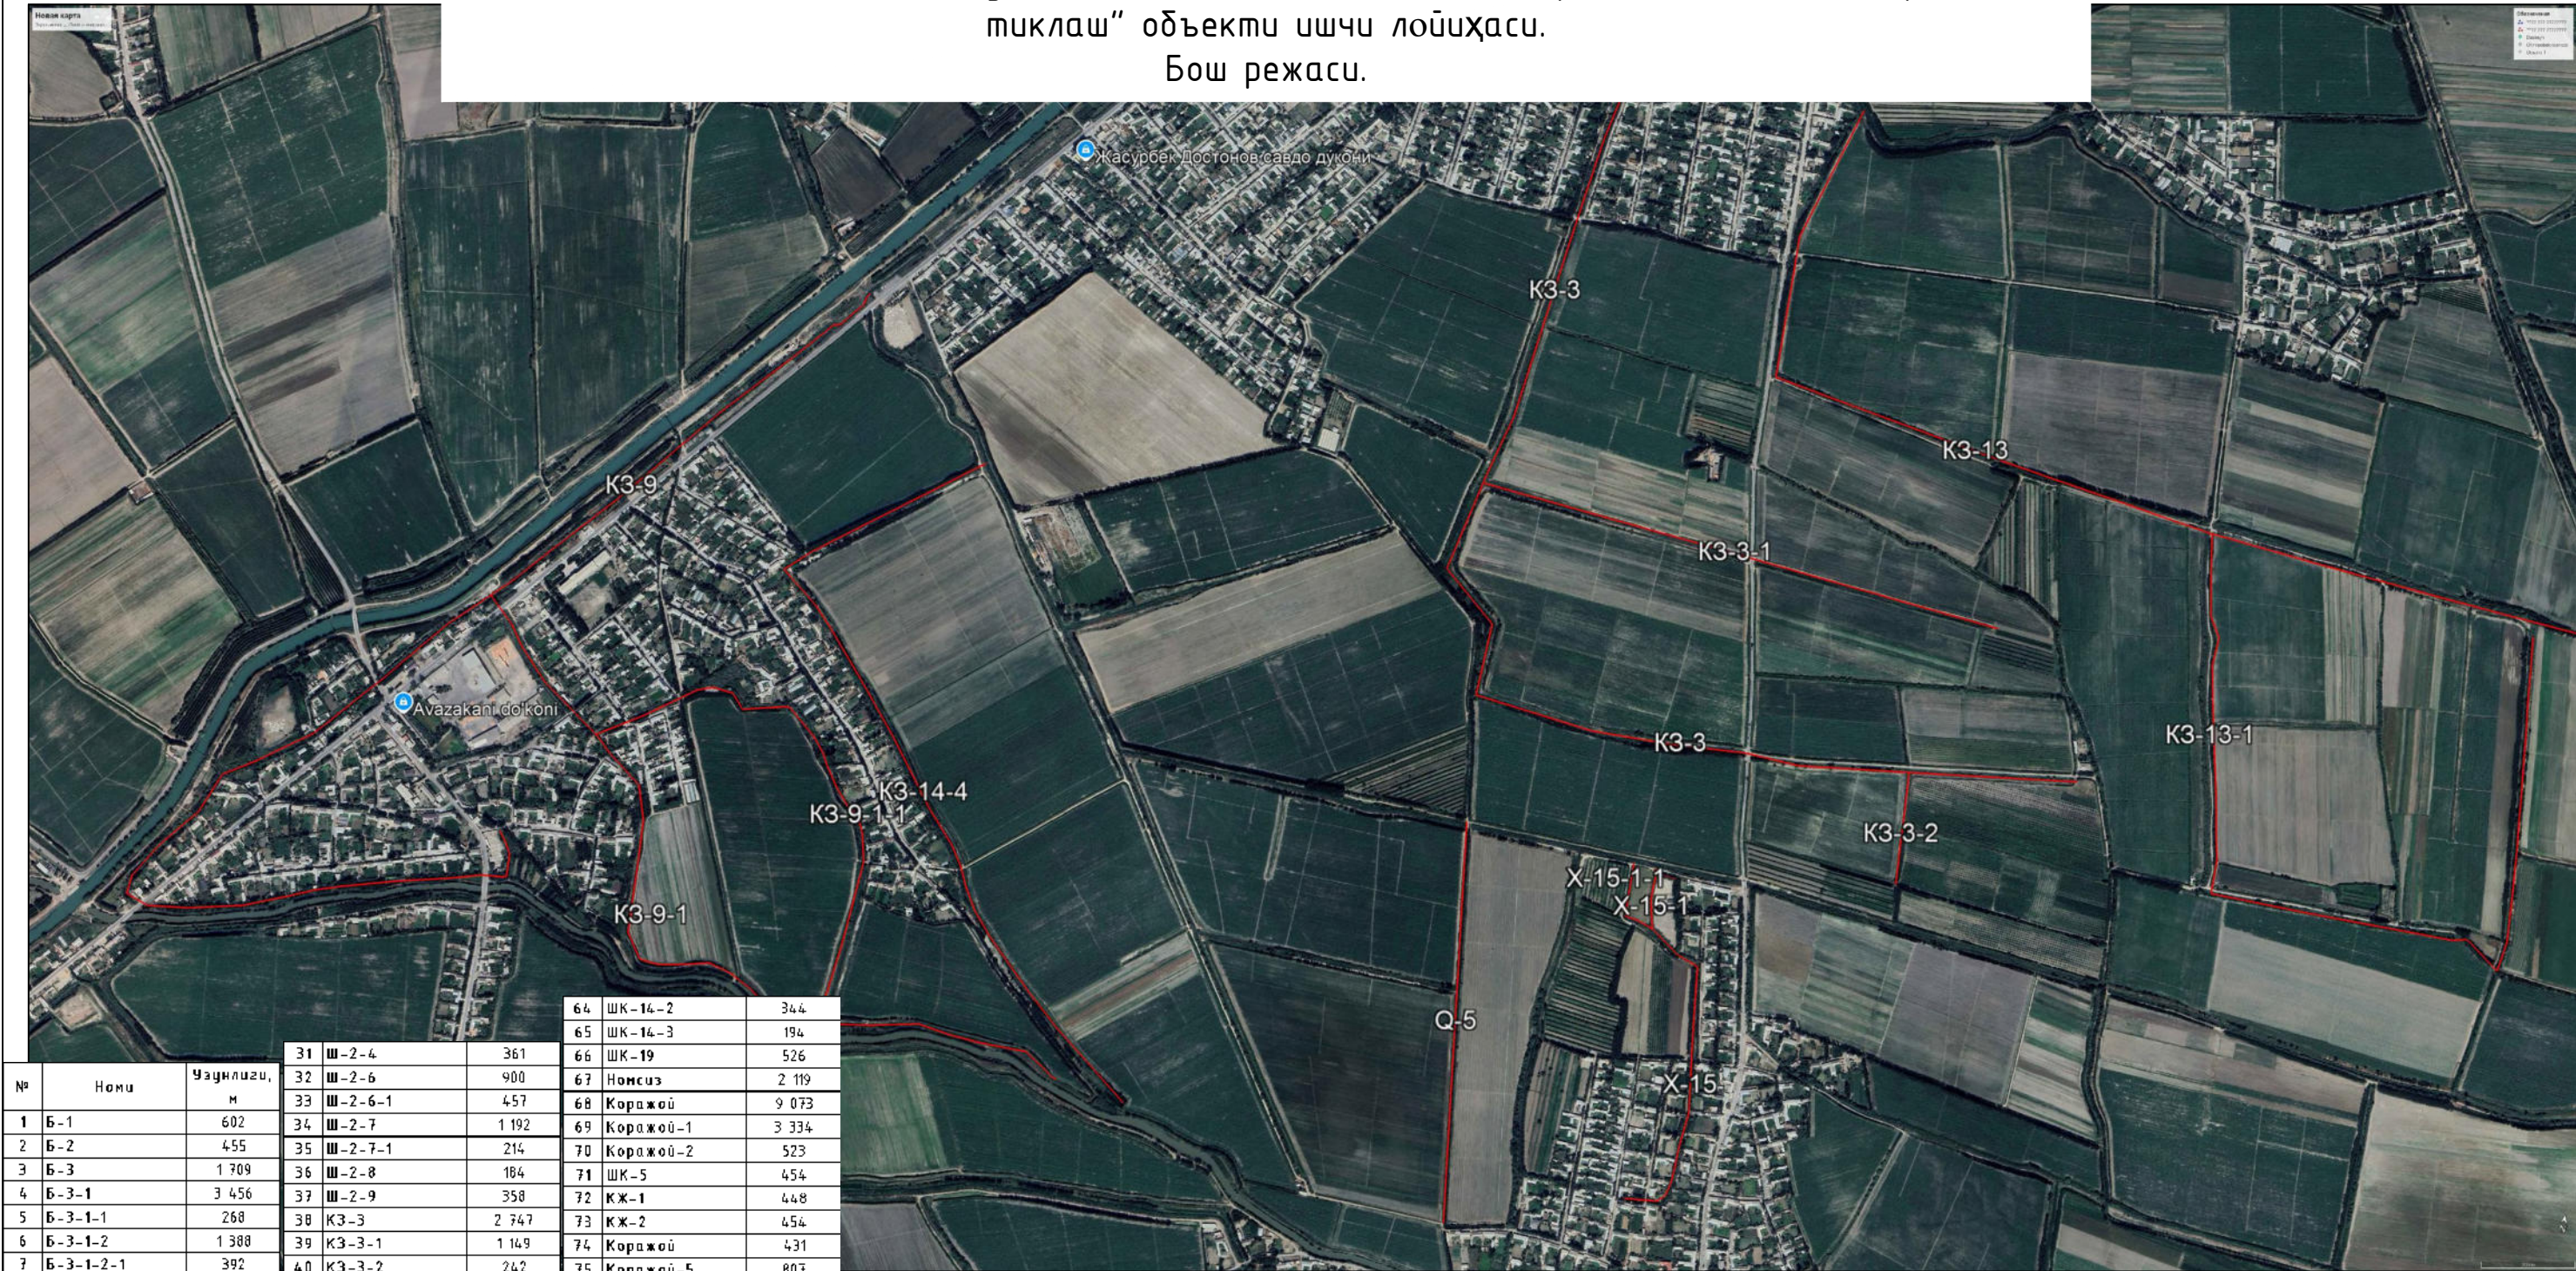

№	Номи	Узунлиги, м	31	Ш-2-4	361	64	ШК-14-2	344
1	Б-1	602	32	Ш-2-6	900	65	ШК-14-3	194
2	Б-2	455	33	Ш-2-6-1	457	66	ШК-19	526
3	Б-3	1 709	34	Ш-2-7	1 192	67	Нонсиз	2 119
4	Б-3-1	3 456	35	Ш-2-7-1	214	68	Коражой	9 073
5	Б-3-1-1	268	36	Ш-2-8	184	69	Коражой-1	3 334
6	Б-3-1-2	1 388	37	Ш-2-9	358	70	Коражой-2	523
7	Б-3-1-2-1	392	38	КЗ-3	2 747	71	ШК-5	454
8	Б-3-1-3	448	39	КЗ-3-1	1 149	72	КЖ-1	448
9	Б-3-1-4	94	40	КЗ-3-2	242	73	КЖ-2	454
10	Б-3-1-5	250	41	КЗ-3-9	2 981	74	Коражой	431
11	Б-3-2	150	42	КЗ-9-1	1 867	75	Коражой-5	807
12	Б-4	860	43	КЗ-9-1-1	1 191	76	Халифачек-15	895
13	Б-4-1	419	44	КЗ-11	3 461	77	Халфачек-15-1	140
14	Б-4-1-1	414	45	КЗ-11-1	359	78	Халфачек-15-1-1	50
15	Б-5	1 006	46	КЗ-11-2	252	79	Бешкетмон	4 858
16	Б-6	778	47	КЗ-11-3	227	80	БК-1	185
17	Б-7	952	48	КЗ-11-3-1	403	81	БК-2	379
18	Б-7-1	177	49	КЗ-11-4	280	82	БК-4	790
19	Б-8	550	50	КЗ-11-5	470	83	БК-5	736
20	Б-8-1	375	51	КЗ-14-4	1 842	84	БК-6	599
21	Б-9	555	52	КЗ-18	2 528	85	БК-7	1 233
22	Б-9-1	581	53	КЗ-18-1	2 165	86	БК-7-1	740
23	Б-10	871	54	КЗ-19	2 967	87	БК-7-2	523
24	Б-10-1	570	55	КЗ-19-1	1 301	88	БК-8	850
25	Ш-2	2 961	56	КЗ-19-1-1	554	89	БК-9	241
26	Ш-2-1	419	57	КЗ-19-1-2	583	90	ДМ-2	1 946
27	Ш-2-2	394	58	КЗ-19-2	684	91	ДМ-2-1	283
28	Ш-2-3	224	59	ШК-5-5	1 524	92	ДМ-2-2	405
29	Ш-2-3-1	485	60	ШК-11	3 547	93	ДМ-3-2	437
30	Ш-2-3-1-1	159	61	ШК-11-1	1 171	94	ДМ-3-2-1	331
			62	ШК-14	2 427	95	ДМ-3-4	1 119
			63	ШК-14-1	266	96	ДМ-3-4-1	223
				Всего	99 270	97	ДМ-2-5	784

					“Андижон вилояти Балиқчи туманидаги “Бешкетмон” коллекторини тизимли таъмирлаш ва тиклаш” объекти ишчи лойиҳаси.			
Изм	Лист	Ф.И.О.	Подпись	Дата	ГЕН ПЛАН	Лист	Листов	Масштаб
ГИП:		Х.Абдухоликов				3	3	
Исполнит		У.Йулдошев						
Топограф		Ю.Ганиев						
						ООО “INVEST PROYEKT UNIVERSAL”		